
REBUS — plan du rez-de-chaussée, état des lieux (actuel)

Bâtiment REBUS, FarmLab La Vauzelle — échelle 1/100 (A3) — 17/10/2026

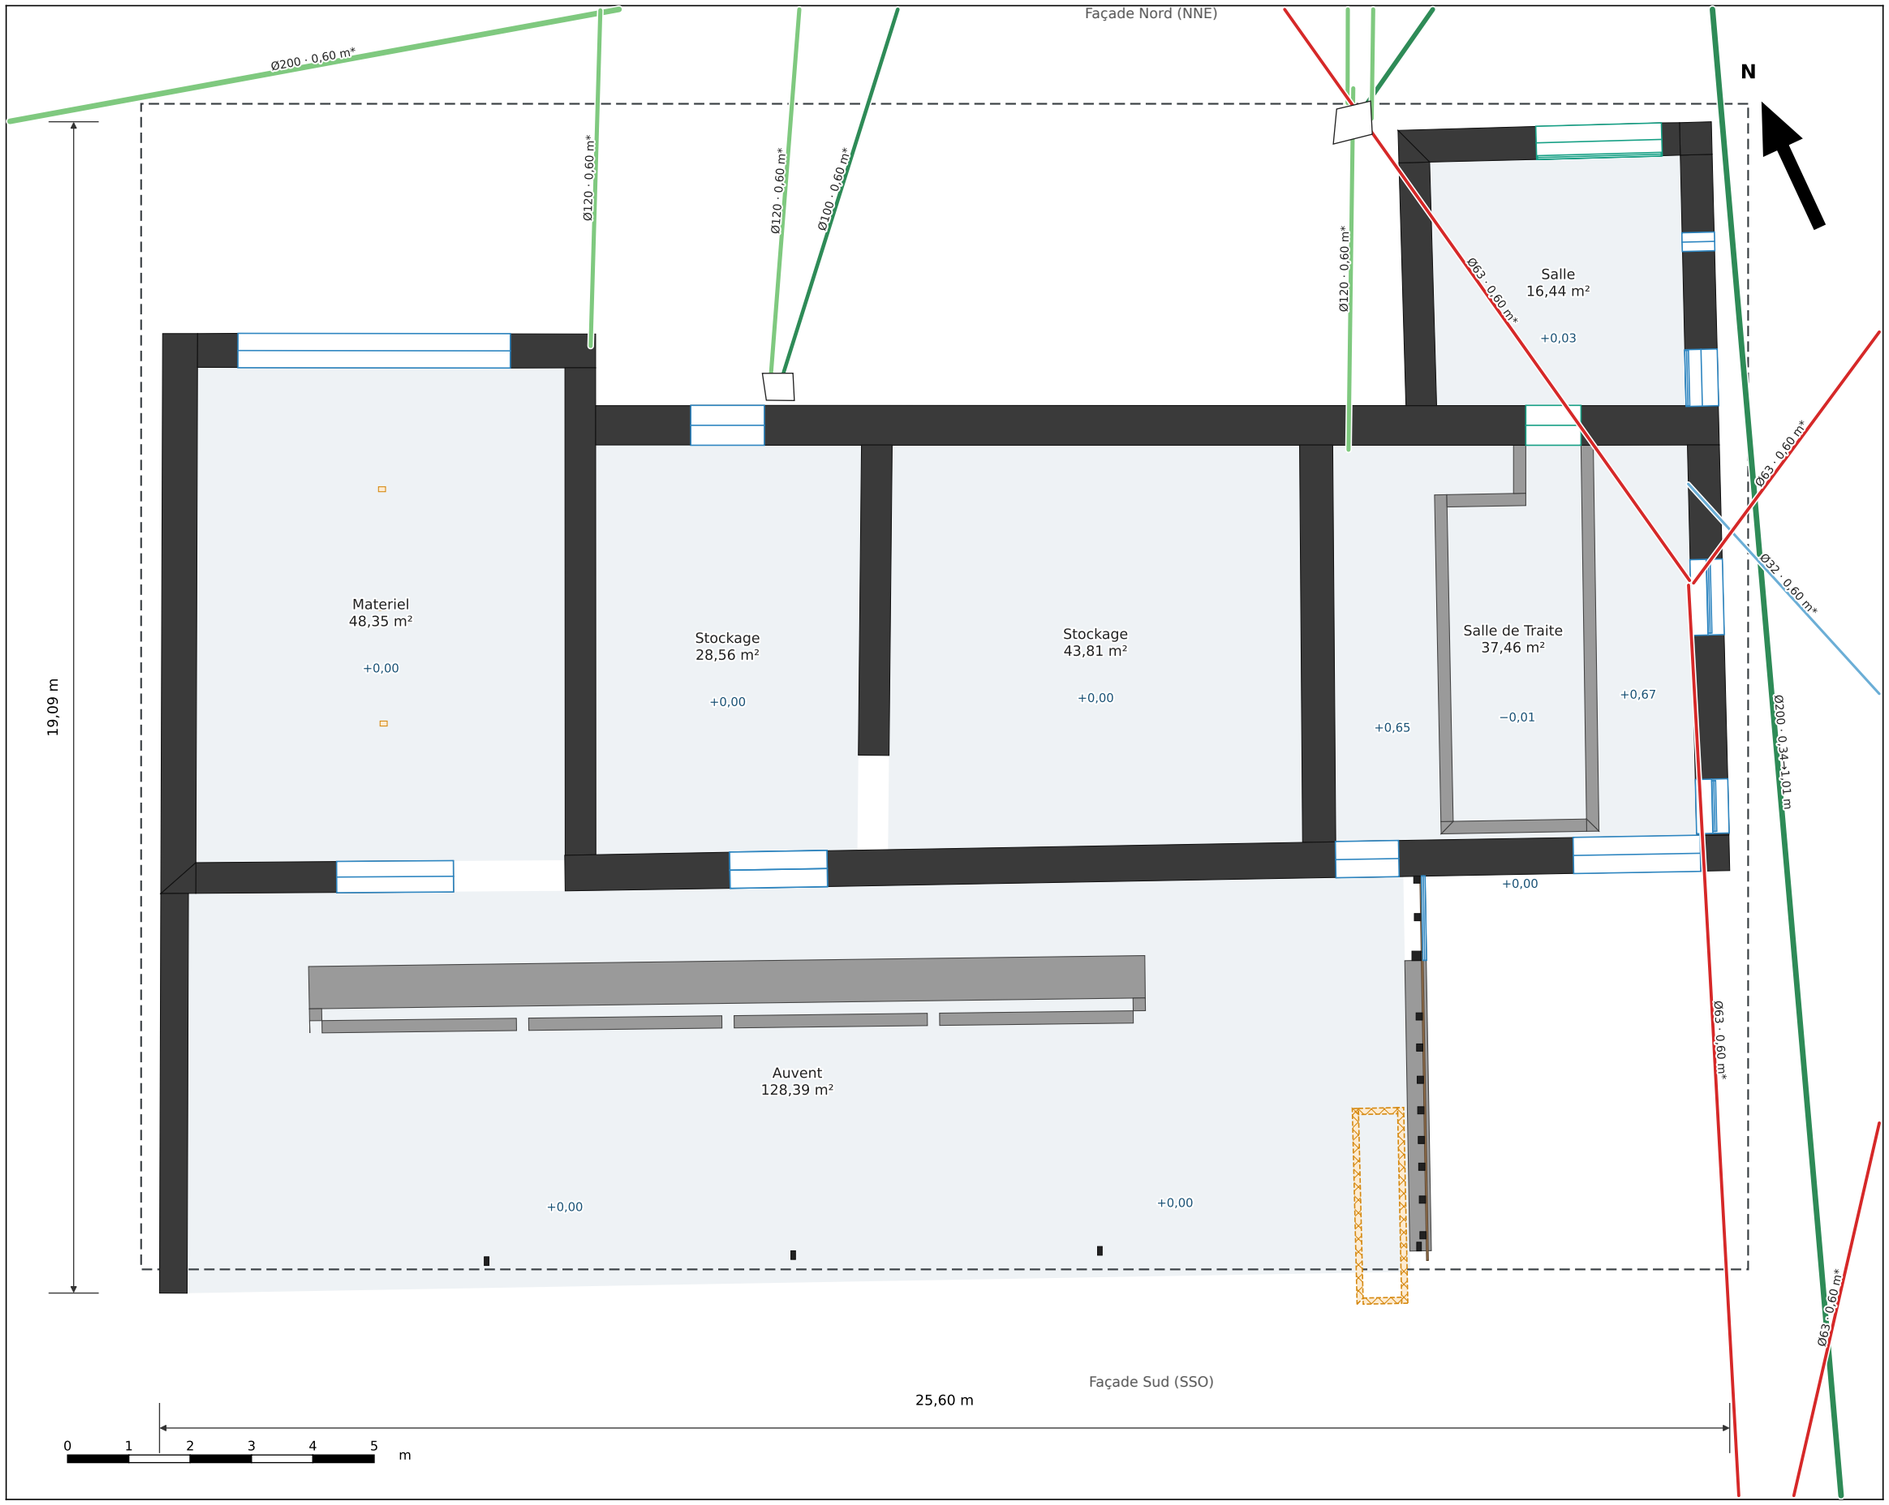

Légende

- Mur existant
- Muret, soubassement existant
- Support de menuiserie
- À démolir
- Affectation actuelle
- Bardage bois
- Fenêtre, baie
- Porte
- Poteau
- Débord de toiture
- +0,37 : cote de sol (m, zéro du plan d'architecte)

Réseaux enterrés

- Eaux pluviales (existant)
- EP / EU (travaux)
- Eau du puits
- Adduction d'eau potable
- Électricité (TPC)
- Électricité solaire
- Regard
- Fosse
- Ø diamètre (mm) · profondeur (m)
- * profondeur par défaut (0,60 m)

Sources : plans MG Architecture (Saintes), relevé SIG SCI Les Chênes Verts, IGN (orthophotographie, LiDAR HD). Profondeurs des réseaux indicatives : 0,60 m par défaut quand rien n'est relevé.