
SCI Les Chênes Verts — plan de masse

Site de La Vauzelle, état projet (REBUS) — échelle 1/1000 (A3) — 17/10/2026

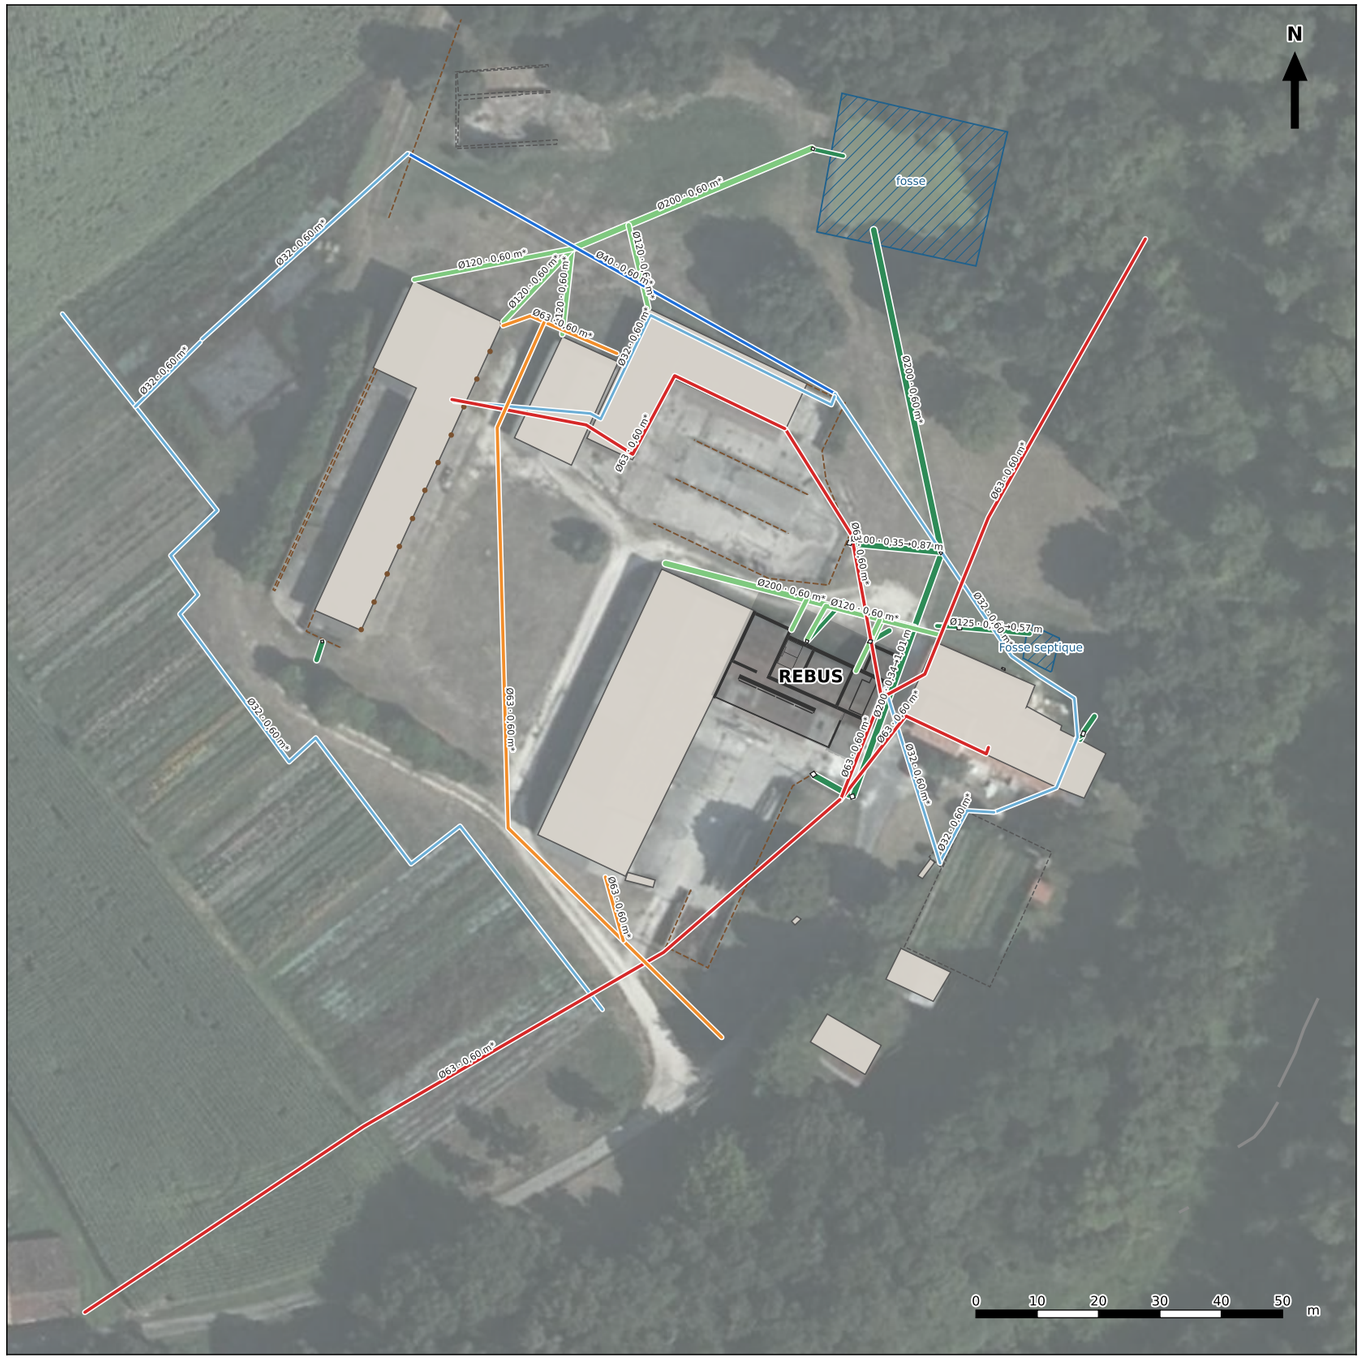

Légende

- Bâtiment existant
- Ruine, potager
- Murs du REBUS (projet)
- Toiture bac acier RAL 7016
- Prolongement de l'appentis
- Clôture
- Mur en pierres sèches

Réseaux enterrés

- Eaux pluviales (existant)
- EP / EU (travaux)
- Eau du puits
- Adduction d'eau potable
- Électricité (TPC)
- Électricité solaire
- Regard
- Fosse

Ø diamètre (mm) · profondeur (m)

* profondeur par défaut (0,60 m)

Coordonnées : Lambert 93 (EPSG:2154)
moins (406 300 ; 6 532 400).
Nord du quadrillage Lambert 93.

Sources : plans MG Architecture (Saintes), relevé SIG SCI Les Chênes Verts, IGN (orthophotographie, LiDAR HD). Profondeurs des réseaux indicatives : 0,60 m par défaut quand rien n'est relevé.